



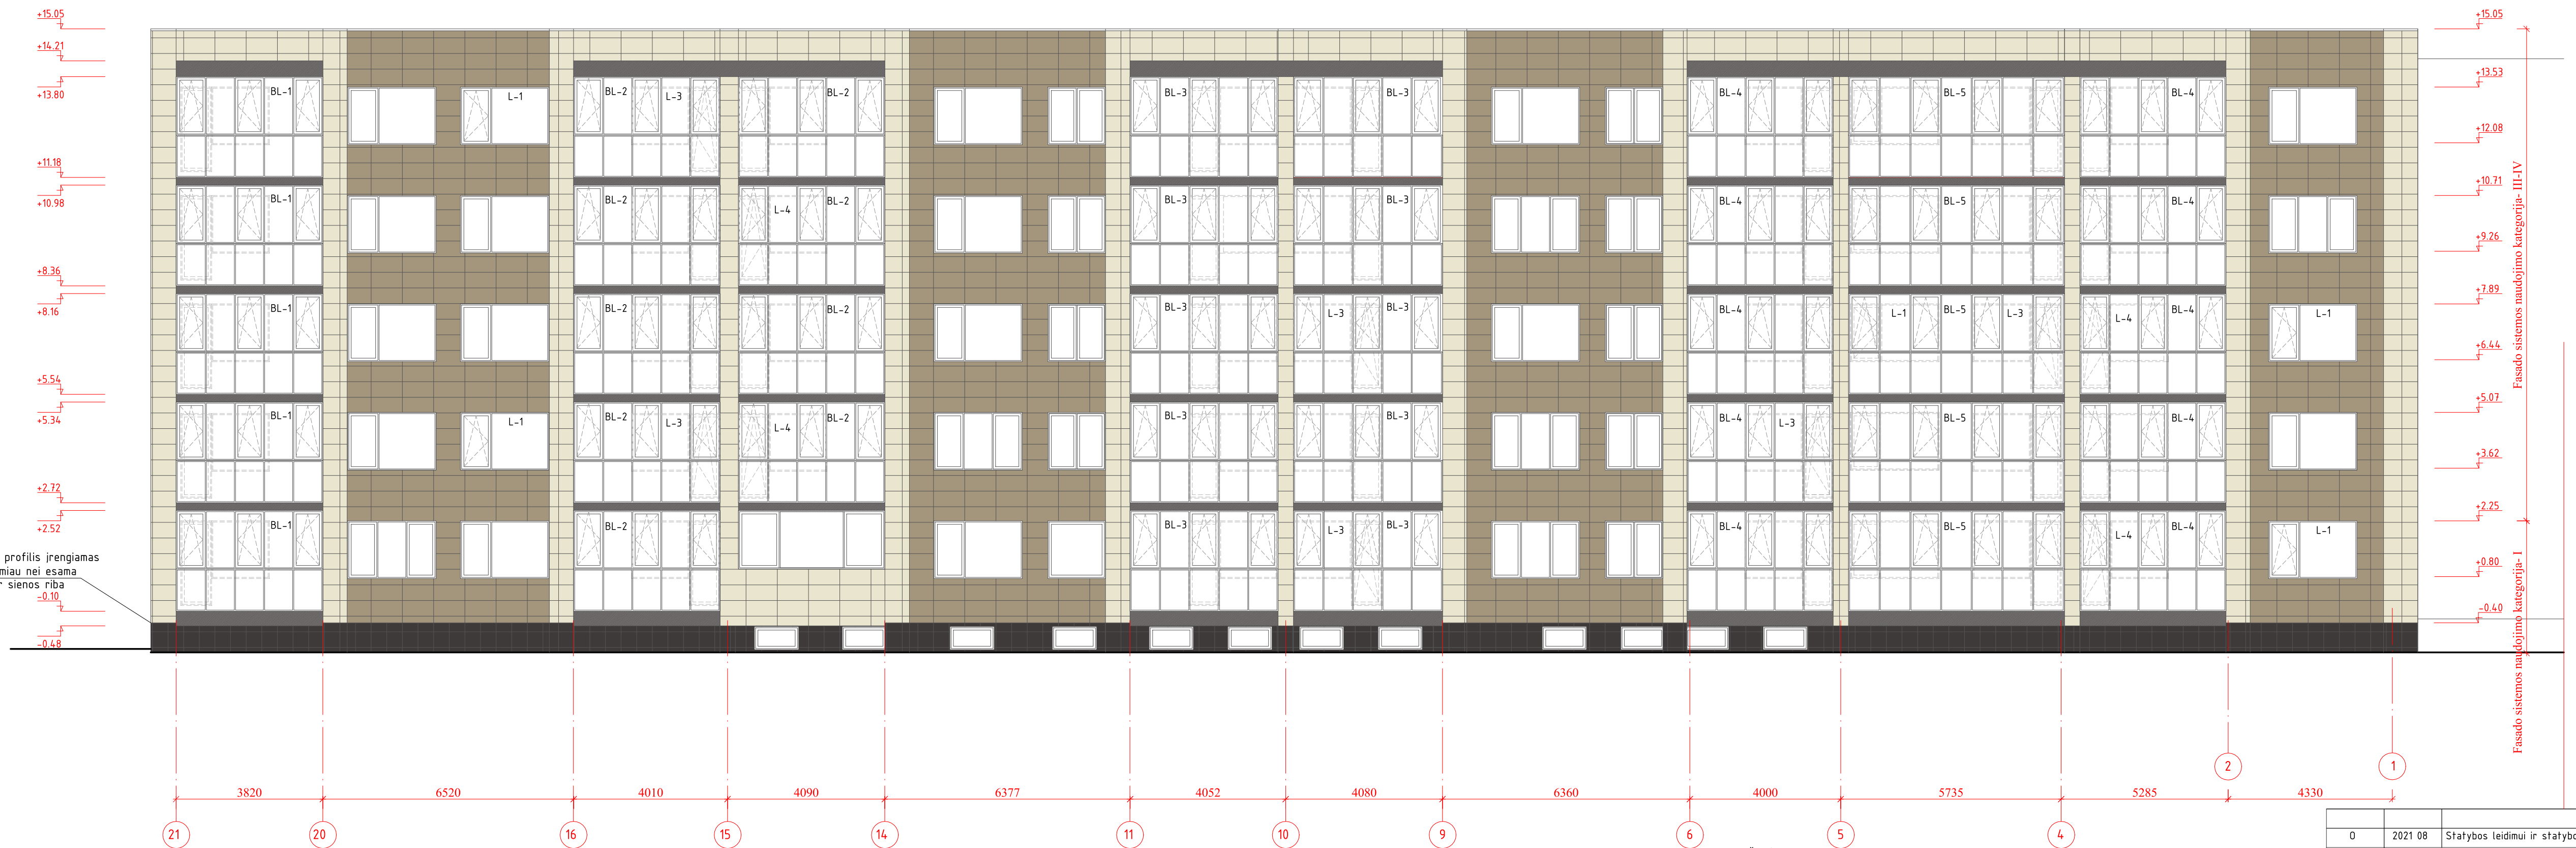



SUTARTINIS ŽYMĖJIMAS	
	Akmens masės plytelės 600x300mm, spalva artima RAL 1013
	Akmens masės plytelės 600x300mm, spalva artima RAL 1019
	Klinkerio plytelės 300x300mm, spalva artima RAL 8019
	Palangės, apskardinimas, durys ir kiti metalo gaminiai- dažytos skardos, RAL 8019
	Angokraščiai skardinami skardos lankstiniais, spalva artima RAL 1013
	Balkonų sienos ir angokraščiai, lubos balkono viduje, tambūro sienos- tinkuojami, dažomi RAL1013

0	2021 08	Statybos leidimui ir statybos darbas	Statinio projekto pavadinimas	
Kval. patv. dok. Nr.	UAB "INŽINERINGS"		DAUGIABŪČIO GYVENAMOJO NAMO VEISIEJŲ G. 30, DRUSKININKAI, ATNAUJINIMO (MODERNIZAVIMO) PROJEKTAS	
3135	PV	A.Kazlauskas	Dokumento pavadinimas	
A1937	SA PDV	G.Dabravolskiene	Fasadai tarp ašių 1-21 ir 21-1 M 1:100	
LT		Užsakovas	Dokumento žymuo	
		UAB „DRUSKININKŲ BUTŲ ŪKIS“	2021-CP0176868-TOP-SP,SA-05	
			LAPAS	LAPŲ
			1	1

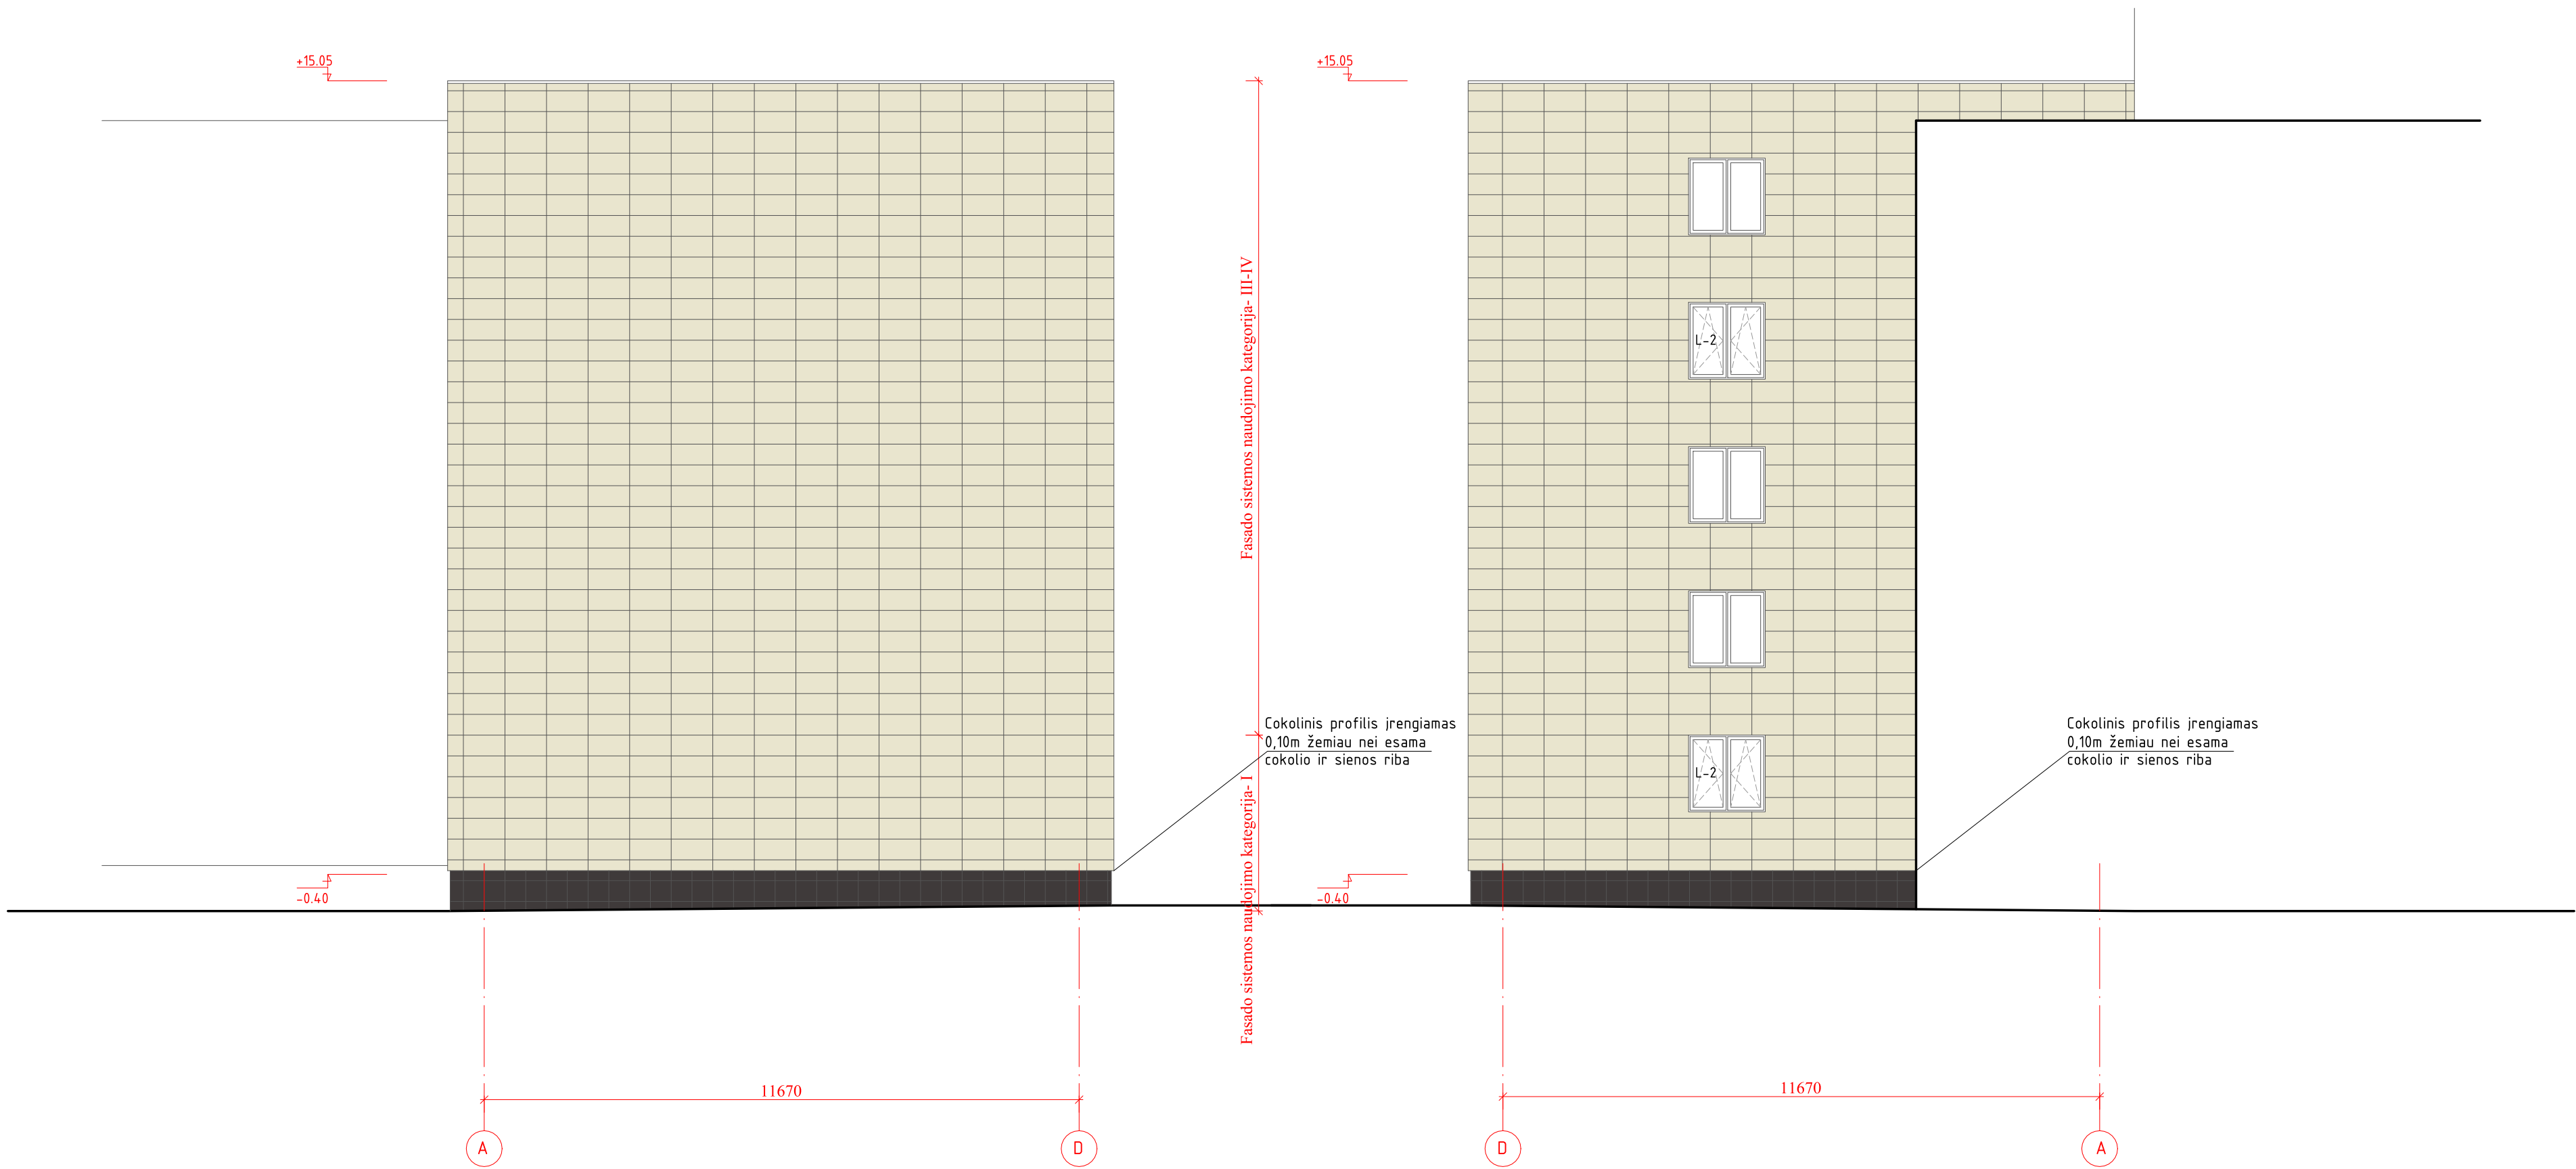

- PASTABOS:
1. Išmatavimai duoti milimetrais, altitudės – metrais.
 2. Matmenis ir altitudės būtina tikslinti vietoje. Matmenis tikslinti vietoje, prieš atliekant montavimo darbus bei užsakant gaminius.
 3. Brėžiniuose radus neatitikimų, sprendinius derinti su projektuotojais.
 4. Privaloma laikytis sistemos atsparumo smūgiams reikalavimų įvertinus sistemos naudojimo kategoriją pagal vietą fasade ir aplinkos situaciją (vadovaujantis STR 2.04.01:2018, Pastatų atitvaros. Sienos, stogai, langai ir išorinės įėjimo durys“sk.IV). Sistemos atsparumo smūgiams kategorijas pateikia sistemos gamintojas.
 5. Jei pastato atitvarose įrengtos deformacinės siūlės, jose pačiose vietose turi būti įrengtos sistemos deformacinės siūlės.
 6. Prieš pradėdami sienų šiltinimo darbus, paruošiami fasadai užtaisomos ištrupėjusios siūlės, atstatomas jų hermetiškus.
 7. Spalviniai fasadų sprendimai turi būti suderinti su projekto architektu ir Druskininkų rajono savivaldybės vyr.architektu. Spalviniai sprendimai parenkami pagal apšiltinimo sistemos tiekėjo pateiktus fasadų spalvynus, kitų fasaduose naudojamų medžiagų gaminių spalvynus. Fasadų apdailos spalvos nurodytos pagal RAL spalvyną, konkrečią apdailos medžiagų spalvą vykdant darbus būtina suderinti su Druskininkų rajono savivaldybės vyr.architektu. Fasadų projektnių sprendimų pakeitimai privalo būti suderinti su projekto architektu ir Druskininkų rajono savivaldybės vyr.architektu.
 8. Brėžinyje nurodytas medžiagas galima keisti analogiškomis, kito gamintojo. Pakeitimus derinti su projekto autoriais. Techniniai parametrai pateikti detalėse gali būti keičiami tik gerinant technines charakteristikas. Detalės gali būti tikslinamos parinkus konkrečią gamintojo sistemą.
 9. Sienų apšiltinimui naudoti tik gamintojo patvirtintą sistemą, kurią turi sudaryti kaip vienas vieno gamintojo statybos produktas, rinkai pateiktas statybos produktų rinkinys (komplektas), turintis ETI ir paženklintas CE ženklu, arba šis rinkinys, turintis NT). Iš atskirų tiekėjų ir gamintojų komplektuoti nesertifikuotą sistemą draudžiama.
 10. Šiltinimo ir apdailos sistemos degumo klasė ne žemesnė nei Bs-1, d-0.
 11. Darbai vykdomi remiantis pridėdomomis tipinėmis detalėmis.
 12. Namų nr. ir vėlavos laikiklis prieš modernizavimo darbus numontuojami, įdėtinės detalės įrengiamos prieš apšiltinimo darbus. Po darbų montuojami tose pačiose arba su pastato administratoriumi aptartose vietose.

SUTARTINIS ŽYMĖJIMAS							
		Akmenų masės plytelės 600x300mm, spalva artima RAL 1013					
		Akmenų masės plytelės 600x300mm, spalva artima RAL 1019					
		Klinkerio plytelės 300x300mm, spalva artima RAL 8019					
		Palangės, apskardinimas, durys ir kiti metalo gaminiai- dažytos skardos, RAL 8019					
		Angokraščiai skardinami skardos lankstiniais, spalva artima RAL 1013					
		Balkono sienos ir angokraščiai, lubos balkono viduje, tambūro sienos- tinkuojami, dažomi RAL1013					
0	2021 08	Statybos leidimui ir statybos darbams					
Kval. patv. dok. Nr.	UAB "INŽINERINGAS"				Statinio projekto pavadinimas		
					DAUGIABUČIO GYVENAMOJO NAMO VEISĖJŲ G. 30, DRUSKININKAI, ATNAUJINIMO (MODERNIZAVIMO) PROJEKTAS		
3195	PV	A.Kazlauskas		Dokumento pavadinimas		LAPAS	LAPŲ
A1937	SA PDV	G.Dabravolskienė		Fasadai tarp ašių A-D ir D-A M 1:100		0	
				Dokumento žymuo			
LT	Užsakovas		2021-CP0176868-TDP-SP,SA-06		1	1	
	UAB „DRUSKININKŲ BUTŲ ŪKIS“						

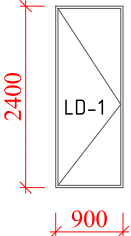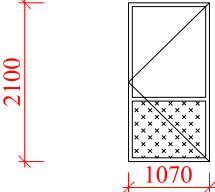NR.	DURŲ TIPAS	KIEKIS	ŽYMĖJIMAS	APRAŠYMAS
1		2 vnt.	LD-1	Metalinės šiltos durys į rūšį- su pritraukėjais ir apvadais, su kojele, su atmušėju, su sandarinančiais tarpikliais, rakinamos cilindrine spyna, kiekvienam butui turi būti skirta po 1 raktą. ; Durų plotis negali būti mažesnis už esamų durų plotį. Matmenis tikslinti vietoje. $UN \leq 1,6 W/m^2K$; 0.90x2,40(h)m 2.16m²
2		4 vnt.	D-1	PVC profilio durys su pritraukėjais ir apvadais, viršutinė dalis įstiklinta saugaus stiklo pakuete, apatinė sustiprinto PVC užpildu, su kojele, su atmušėju, su sandarinančiais tarpikliais; Spalva: balta 1.07x2.10(h)m 2.25m²

PASTABOS durims:

- Žiniaraštyje parodytas gaminių vaizdas iš išorės;
- Matmenys nurodyti milimetrais;
- Brėžiniuose nurodyti angų matmenys. Žiniaraštyje nurodytas gaminių plotas apskaičiuotas pagal angų matmenis. Gaminių ir projektuojamų angų matmenys gali skirtis apie 10%, tikslinama matuojant.
- Gamintojas privalo išmatuoti angas. Gaminių atitikimas vietai yra gamintojo atsakomybė;
- Gaminiai turi būti sertifikuoti LR sertifikavimo centre, atitikti LR galiojančias sandarumo, higienos, akustines ir priešgaisrines normas.
- Įstiklintus blokus turi būti galima saugiai ir patogiai išvalyti iš vidaus ir išorės.
- Užsakovas pagal pastato naudojimo poreikius gali keisti gaminių varstymo kryptis.
- Gamybai naudojamo PVC profilio matomų išorinių sienelių storis ne mažiau nei 2,8mm, nematomų sienelių storis – ne mažiau nei 2,5mm, profilio plotis ne mažiau nei 70 mm.
- PVC profilių gamybai neturi būti naudojami švino pagrindu pagaminti stabilizatoriai.
- Gaminiai turi būti armuoti visu perimetru cinkuoto plieno profilais, kurių sienelės storis ne mažiau nei 1,5mm.
- Gaminuose naudojamos tarpinės turi būti pagamintos iš EPDM, TPR, PCE arba silikono.
- Durų mechaninio patvarumo klasė 6, stiprio 3;
- Keičiant duris keičiami apvadai, slenksčiai, atstatoma vidinių angokraščių apdaila (tinkuojama, glaistoma, dažoma);
- Durys pastatuose turi būti montuojami pagal gamintojo arba kitas jo nurodytas ir viešai paskelbtas instrukcijas.
- Laiptinės durų varčių plotis turi būti nesiauresnis už esamų laiptų plotį.
- Gaminiai statomi į esamas angas, jos nekeičiamos
- Evakuacinių išėjimų durų, pro kurias evakuojasi 50 ir daugiau žmonių, evakuaciniai užraktai parenkami pagal LST EN 179 serijos standarto reikalavimus. Evakuavimui kelių iš pastatų išorinės evakuacinės durys privalo turėti užraktus arba uždarymo mechanizmus, atidaromus iš vidaus.

0	2021 08	Statybos leidimui ir statybos darbams			
Kval. patv. dok. Nr.	UAB "INŽINERINGAS"			Statinio projekto pavadinimas DAUGIABUČIO GYVENAMOJO NAMO VEISIEJŲ G. 30, DRUSKININKAI, ATNAUJINIMO (MODERNIZAVIMO) PROJEKTAS	
3135	PV	A.Kazlauskas		Dokumento pavadinimas	LAIDA
A1937	SA PDV	G.Dabravolskienė		Durų specifikacijos	0
LT	Užsakovas	UAB „DRUSKININKŲ BUTŲ ŪKIS“		Dokumento žymuo	LAPAS LAPŲ
				2021-CP0176868-TDP-SP,SA-08	1 1